
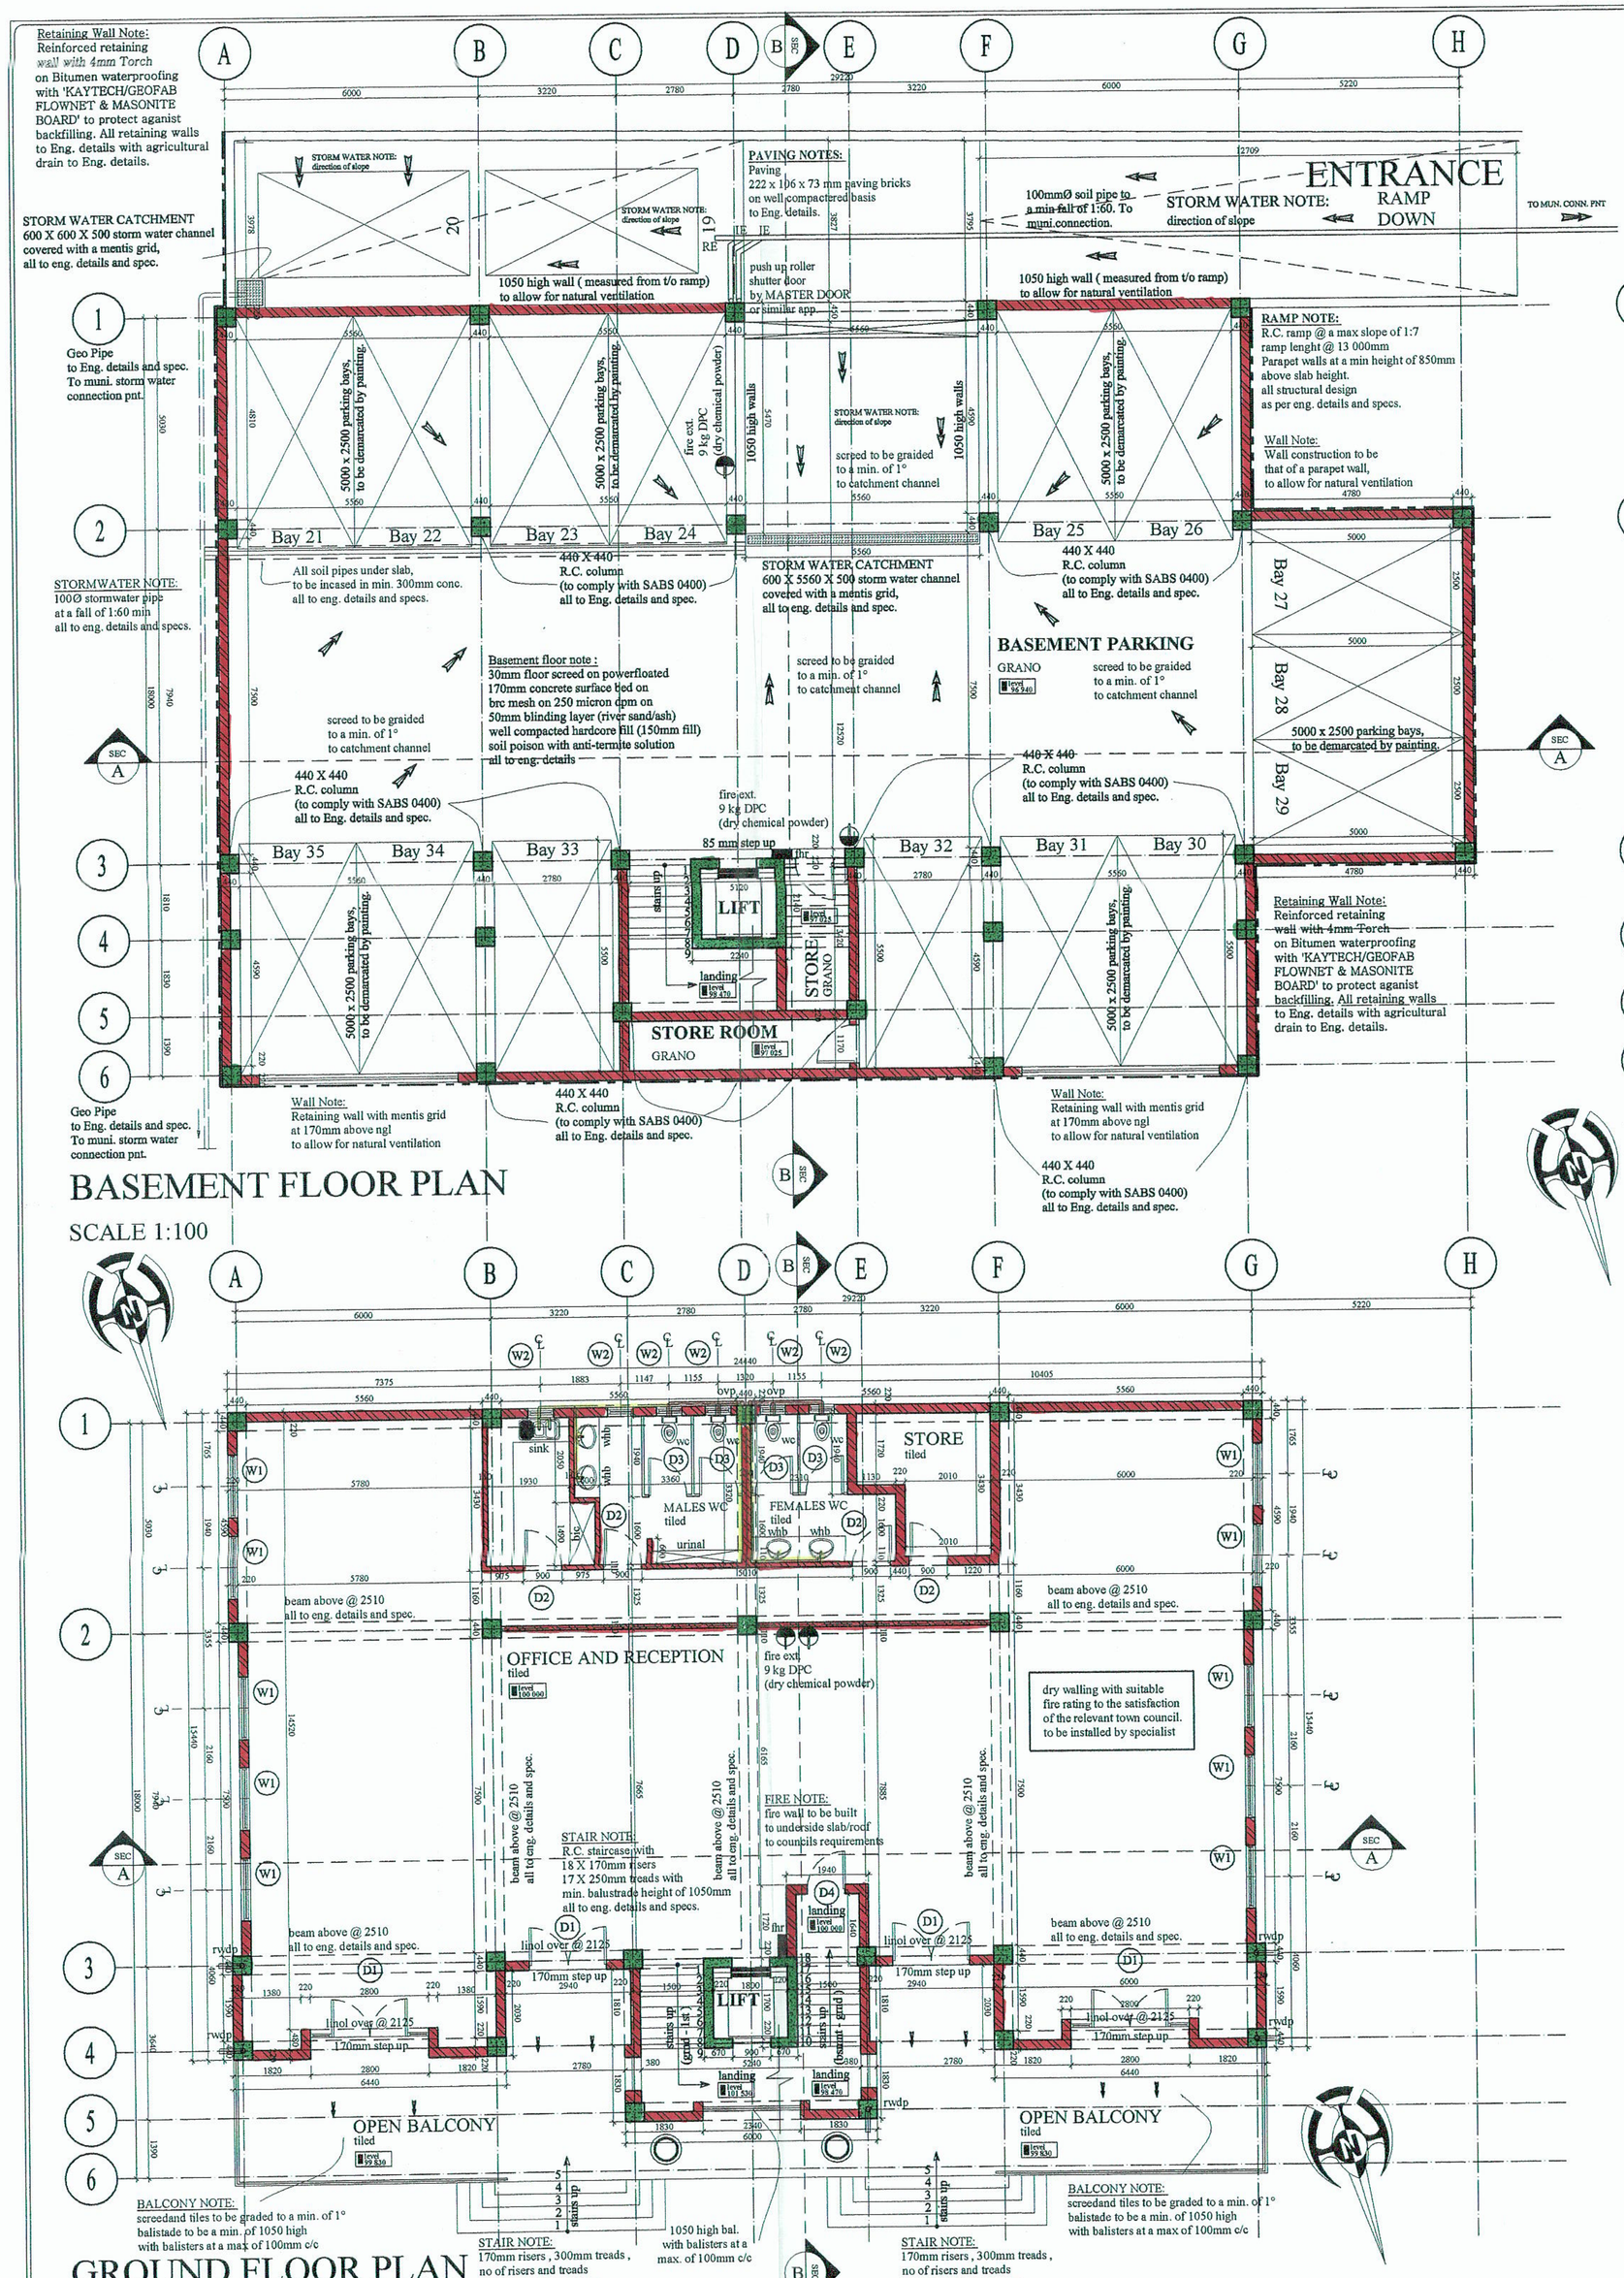


BASEMENT FLOOR PLAN

SCALE 1:100

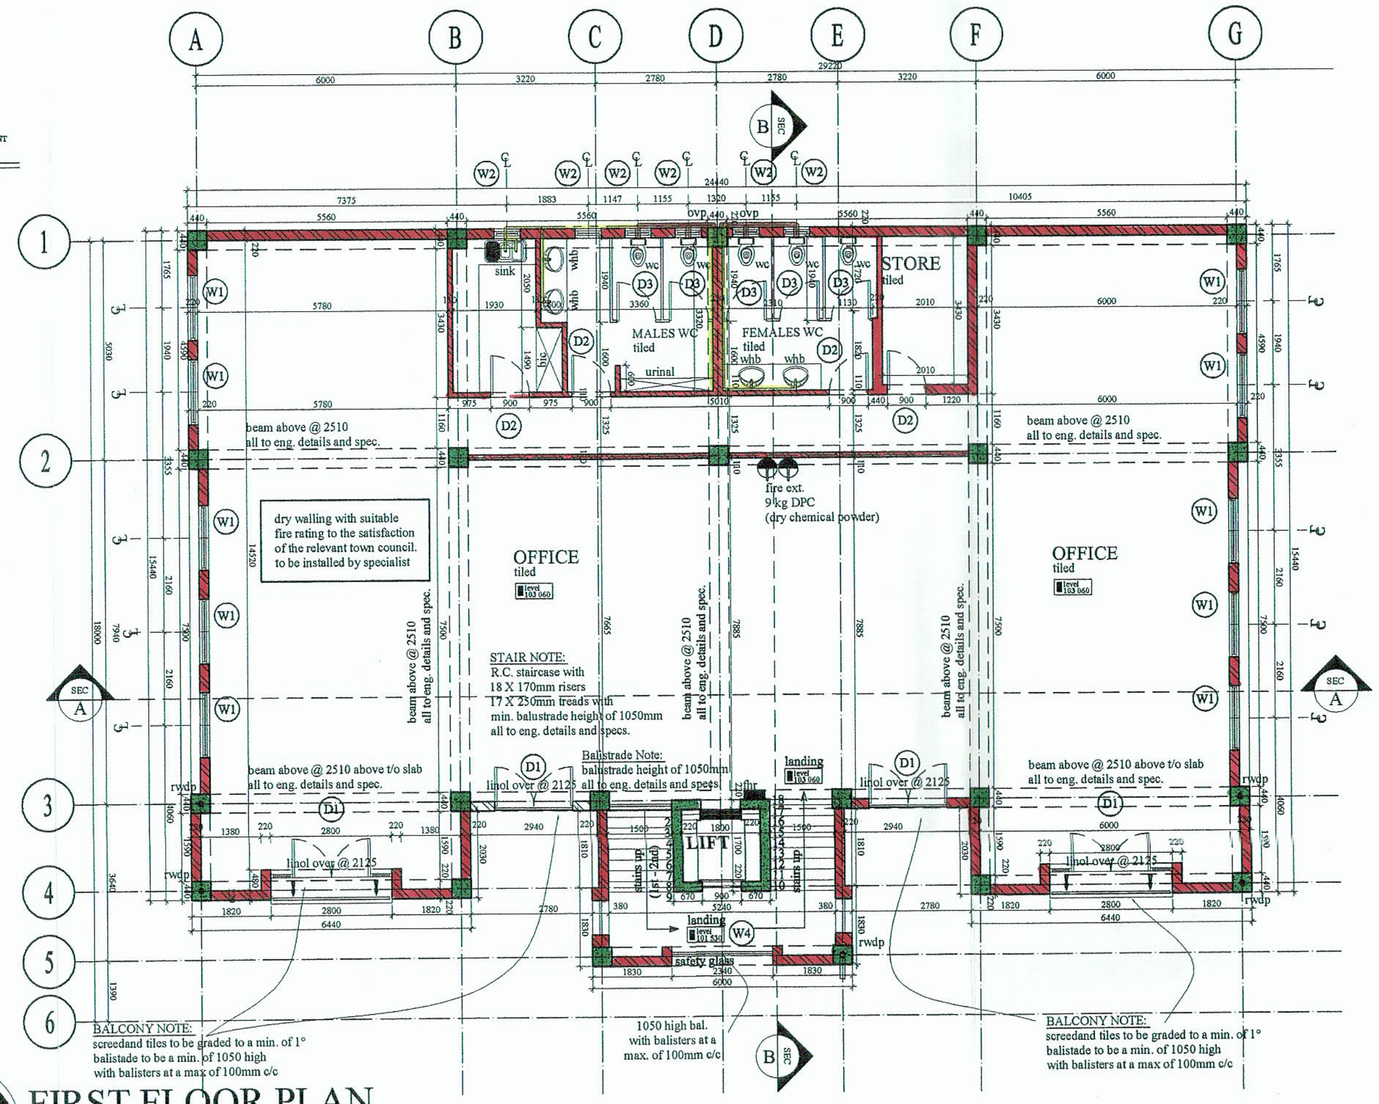


FIRST FLOOR PLAN

SCALE 1:100

GROUND FLOOR PLAN

SCALE 1:100

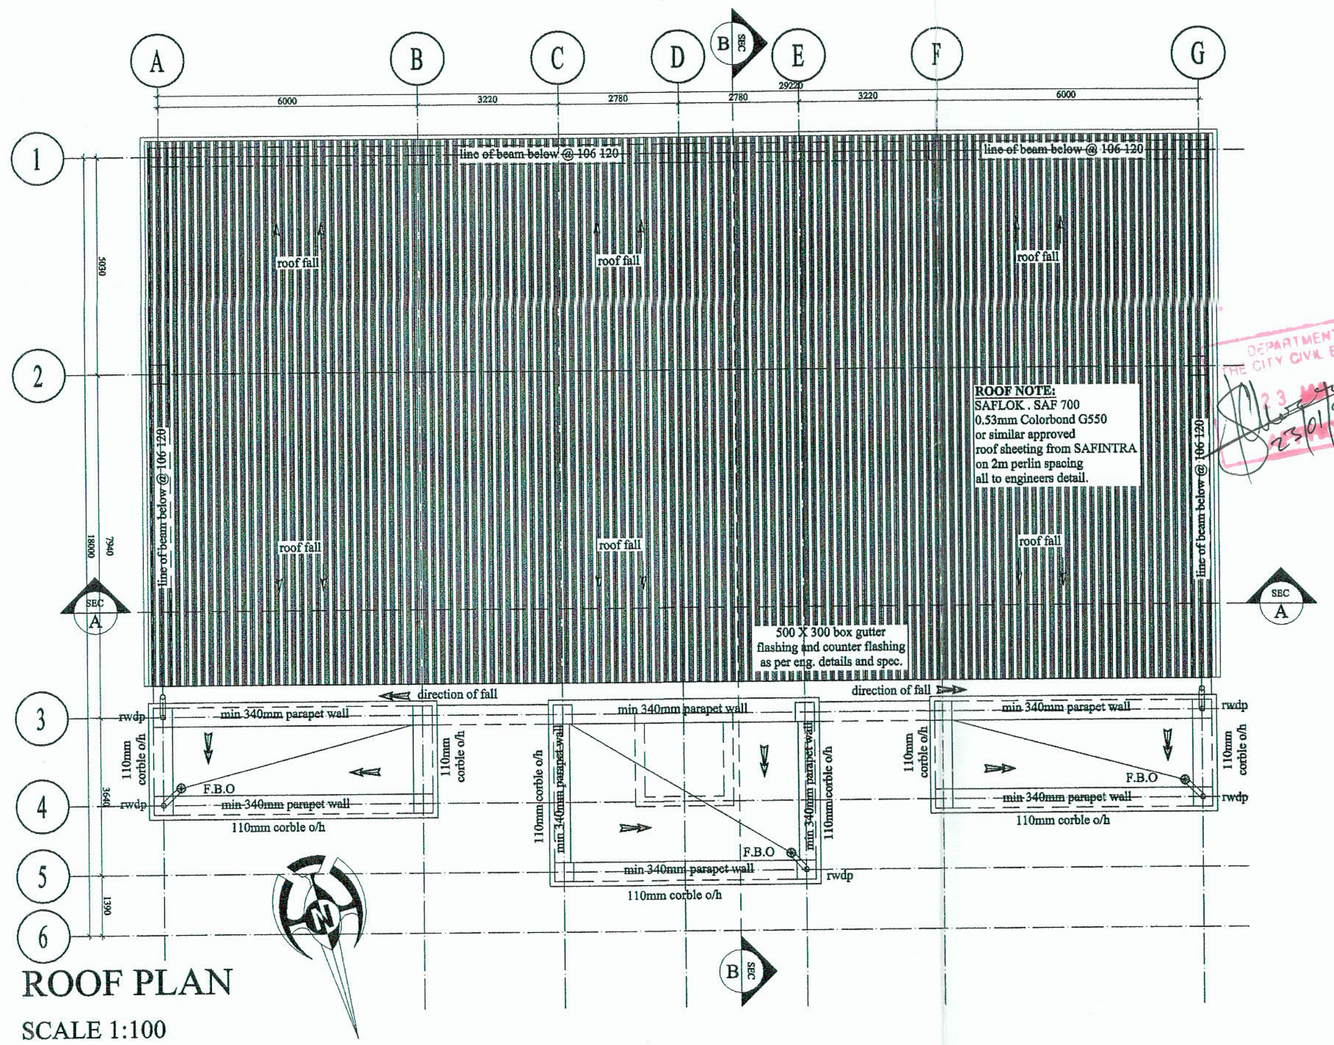

ROOF PLAN

SCALE 1:100

Insight
ARCHITECTURAL DESIGNS
98 RONALD ROAD
LINBRO PARK
SANDTON
2145
Tel: (+2711) 608 1813

PROJECT :
PROPOSED NEW OFFICE ON ERF: 21 / 1577 BEDFORDVIEW EXT 328

DRAWING :
BASEMENT , GROUND, FIRST FLOOR PLANS

DATE : **20/06/2006**

DRAWN BY :

ISSUED : **P. VERVERIS**

PROJ. NO. : **001-BVO-04082005**

DRWG. NO. : **300806 BVO-004**

REVISIONS :

REV.	DESCRIPTION	DATE.
		01
		02
		03
		04
		05

CLIENTS SIGNATURE :

DATE :

ENGINEERS SIGNATURE :

DATE : No 740379

NOTES :

All work to be carried out in strict accordance with the ARCHITECTS instructions.

Top of foundations to be a minimum of 300mm below N.G.L. Vertical DPC to all changes in level's.

Reinforced concrete slab to ENGINEER'S details and specifications.

Waterproofing by specialists.
S.A.B.S. approved bitumen based waterproofing laid with required upturns, onto min. 25mm thick screed. Acrylic based waterproofing to parapet walls & uprisers

All plumbing and drainage installation of sanitary fittings to comply with N.B.R. S.A.B.S. 0400-1990 part P and all relevant local authority by-laws, regulations and requirments.

I.E.'s and R.E.'s to all bends, junctions and changes in direction of soil and waste pipe's.

R.E.'s to all runs exceeding 24m in length.

100Ø GSP. minimum fall 1:60.
100Ø GSP. maximum fall 1:5.

Soil pipes under building's to be encassed in 300mm concrete all round.

All waste fittings to be fitted with re-seal traps.

Staircase specifications to comply with S.A.B.S. 0400-1990 part M.
Balustrades to be minimum 1000mm high.
Balustrades to be minimum 100mm apart.
Risers to be maximum 200mm high.
Treads to be minimum 250mm wide.

THIS DRAWING IS COPYRIGHT.
This is an AUTO CAD generated drawing.
Drawing must not be scaled.
Figured dimensions only may be used.
Dimensions should be verified on site and any discrepancies reported to the ARCHITECTS immediately.

DEPARTMENT OF CITY CIVIL ENGINEER
APPROVED
23 OCT 2007

No building may be used or occupied without a Certificate of Occupancy being issued by the Municipality.
The design and erection of all structural work , including roof trusses and wooden floors must be certified by a professional Structural Engineer.
This plan is only valid for one year from the date of approval.