
graphic Digital COPY

marketing Video

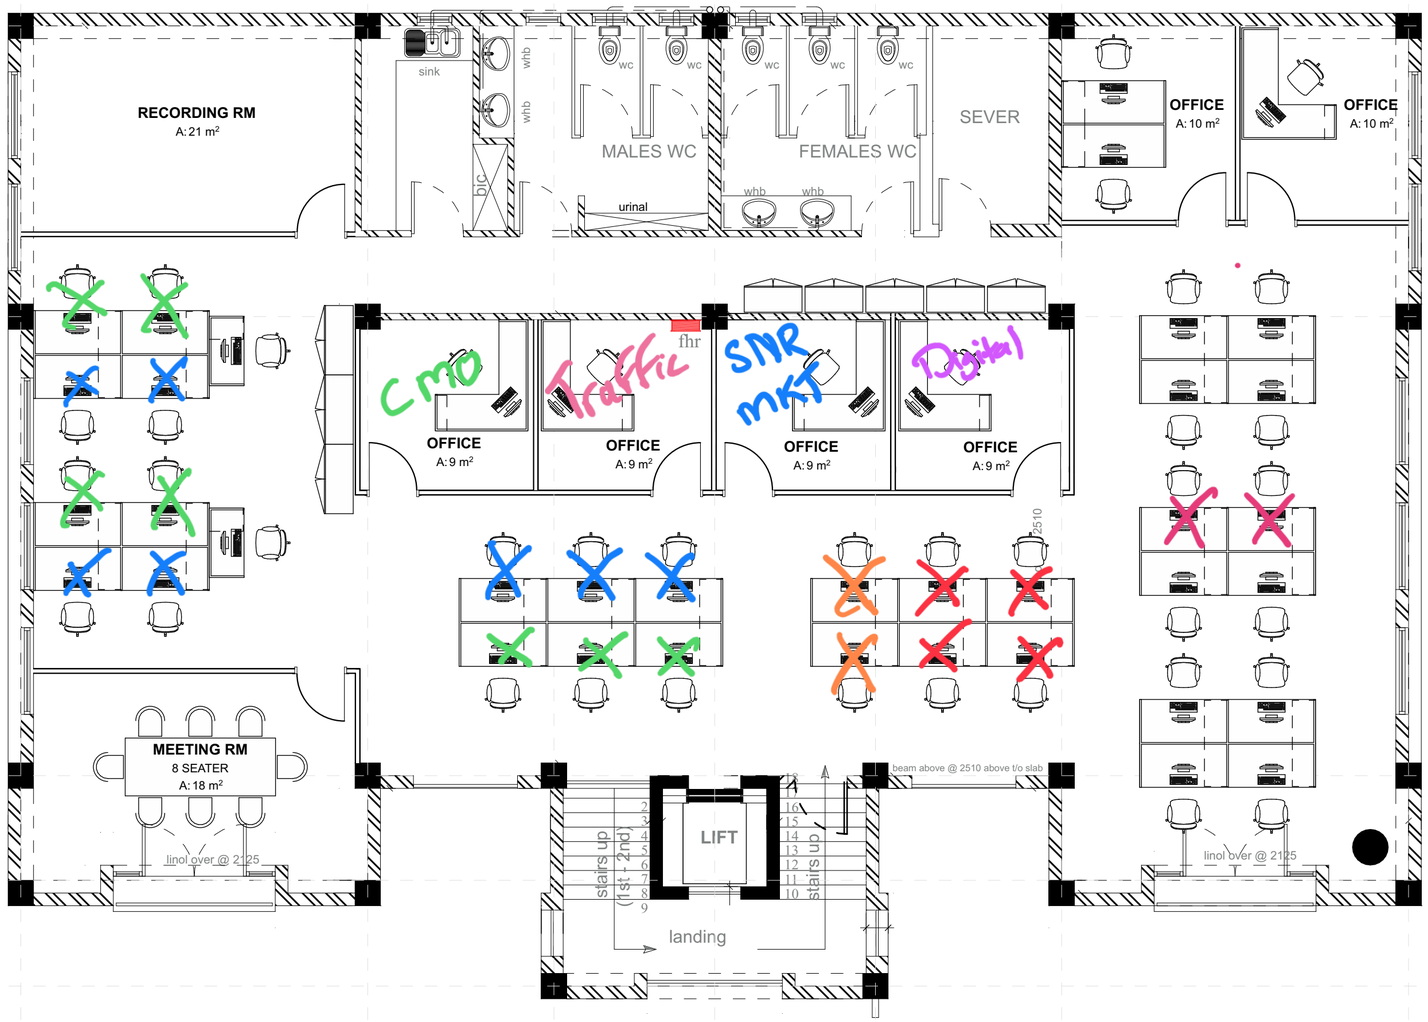

1
2
3
4
5
6

200.01 **FIRST FLOOR - SPACE PLANNING** **1:75**

NOTES

- This drawing is copyright and remains the property of ACDC Dynamics.
- Drawings must not be scaled.
- Figured dimensions to be taken in preference to scaling. Overall dimensions take precedence.
- All dimensions, levels and heights to be checked on site, and any discrepancies to be reported to ACDC Dynamics before any work is put into hand.

REV	DATE	DESCRIPTION
A	20.10.2021	ISSUED FOR COMMENT
B	26.10.2021	ISSUED FOR COMMENT
C	27.10.2021	ISSUED FOR COMMENT
D	29.10.2021	ISSUED FOR COMMENT

ACDC DYNAMICS

PROJECT ARCHITECT / DESIGNER
NMAIO
+2710 202 3000

DRAWN BY
NMAIO
+2710 202 3000

PROJECT

P023
FOR INFINITY BRANDS
ON RILEY ROAD, BEDFORDVIEW

DRAWING TITLE

1ST FLOOR SPACE PLANNING

SCALE	DATE	SHEET SIZE
1:75	2021/10/29	A2

PROJECT No. | DRAWING No.
200.01 **D**