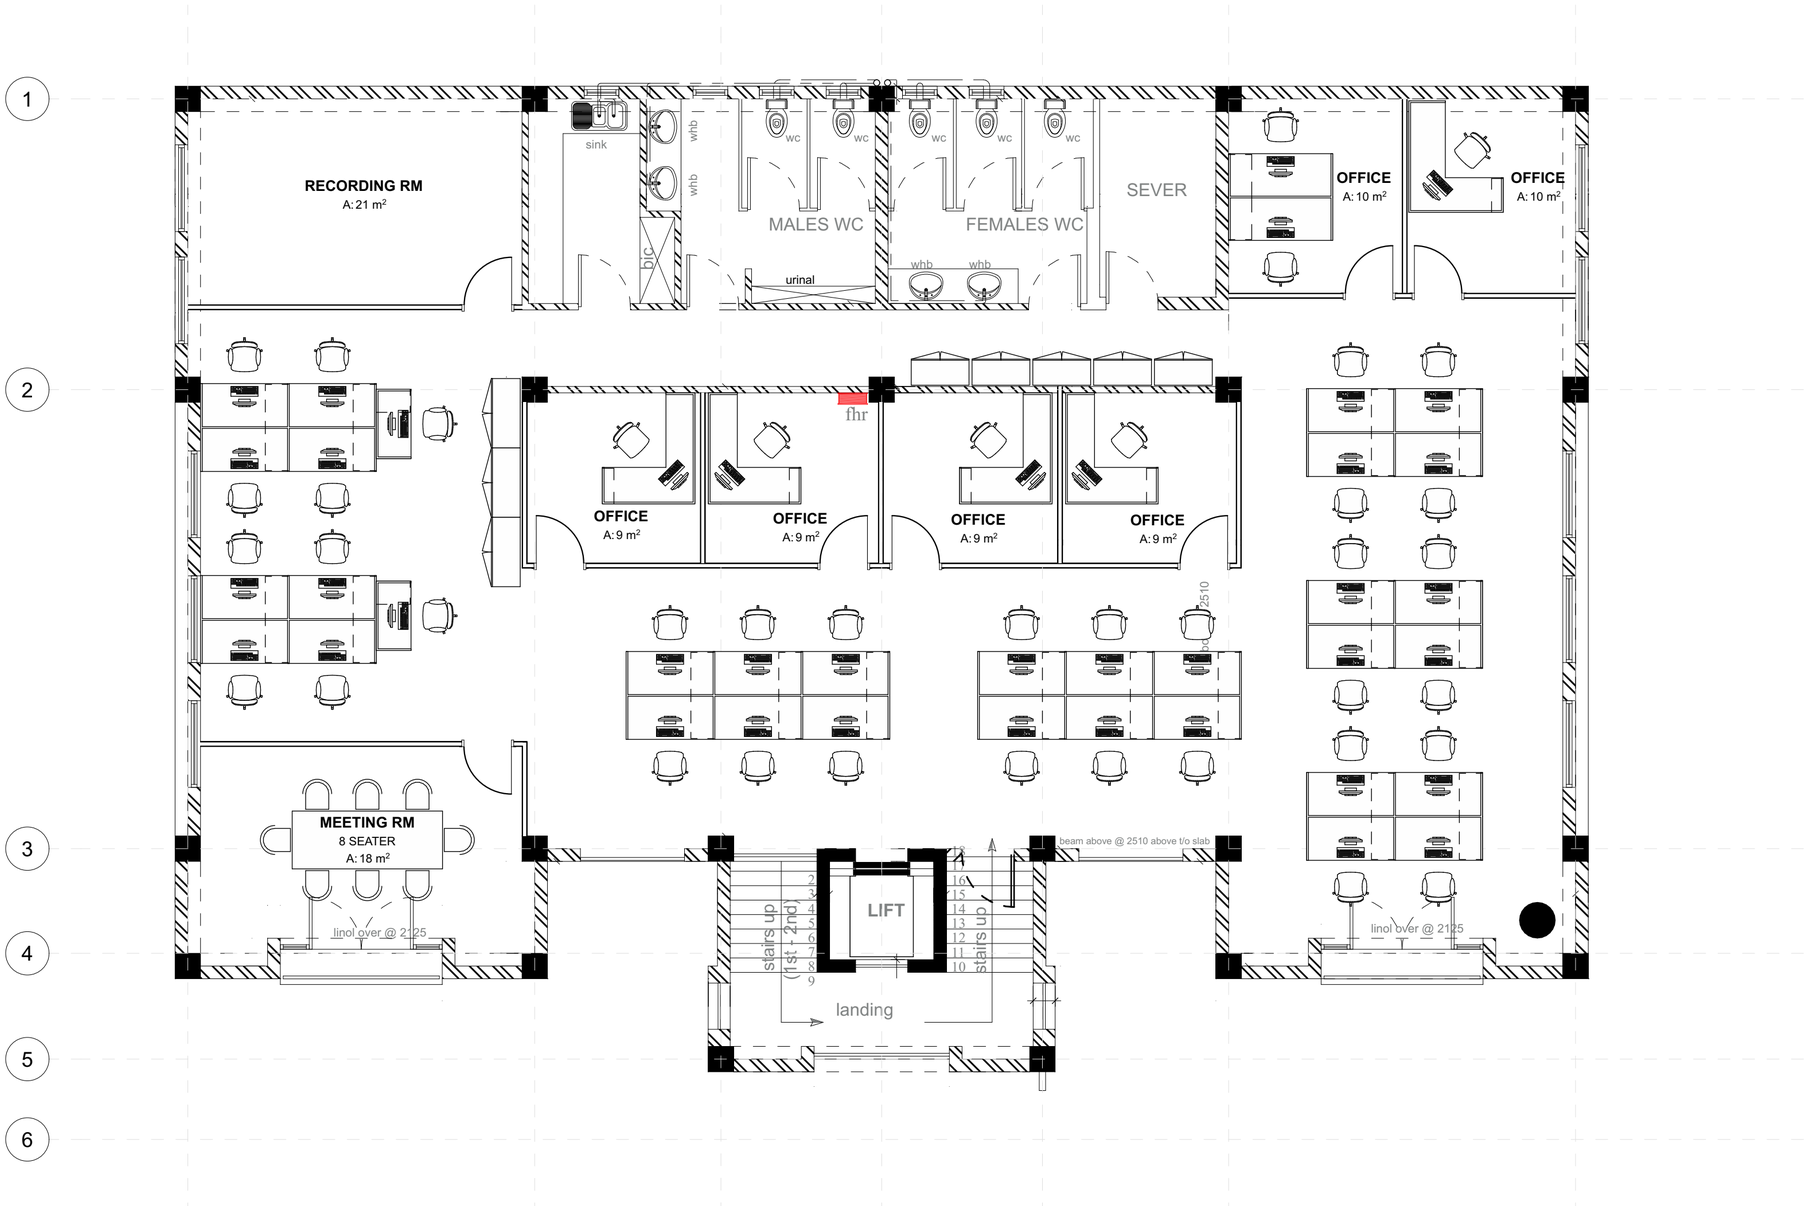



1

2

3

4

5

6

**200.01** **FIRST FLOOR - SPACE PLANNING** **1:75**

## NOTES

- This drawing is copyright and remains the property of ACDC Dynamics.
- Drawings must not be scaled.
- Figured dimensions to be taken in preference to scaling. Overall dimensions take precedence.
- All dimensions, levels and heights to be checked on site, and any discrepancies to be reported to ACDC Dynamics before any work is put into hand.

| REV | DATE | DESCRIPTION |
|---|---|---|
| A | 20.10.2021 | ISSUED FOR COMMENT |
| B | 26.10.2021 | ISSUED FOR COMMENT |
| C | 27.10.2021 | ISSUED FOR COMMENT |
| D | 29.10.2021 | ISSUED FOR COMMENT |

ACDC DYNAMICS

PROJECT ARCHITECT / DESIGNER
NMAIO
+2710 202 3000

DRAWN BY
NMAIO
+2710 202 3000

PROJECT

**P023**
FOR INFINITY BRANDS
ON RILEY ROAD, BEDFORDVIEW

DRAWING TITLE

1ST FLOOR SPACE PLANNING

| SCALE | DATE | SHEET SIZE |
|---|---|---|
| 1:75 | 2021/10/29 | A2 |

PROJECT No. | DRAWING No.
**200.01** **D**